内部仕上表

室名	床	巾木	壁	天井	天井高
売場	長尺塩ビシート t2.0	ビニル幅木 H60	PB t12.5 ビニルクロス	岩綿吸音板 t9.0	2700
レジカウンター	長尺塩ビシート t2.0	ビニル幅木 H60	PB t12.5 ビニルクロス	岩綿吸音板 t9.0	2700
通路	磁器質タイル 300角	ビニル幅木 H60	PB t12.5 ビニルクロス	PB t9.5 塗装	2400
バックヤード	防塵塗装	なし	PB t12.5 塗装	直天井	2600
事務所	タイルカーペット	ビニル幅木 H60	PB t12.5 ビニルクロス	岩綿吸音板 t9.0	2500
休憩室	長尺塩ビシート t2.0	ビニル幅木 H60	PB t12.5 ビニルクロス	PB t9.5 ビニルクロス	2400
トイレ	長尺塩ビシート t2.5	ソフト幅木 H100	ケイカル板 t6.0 塗装	ケイカル板 t6.0 塗装	2300

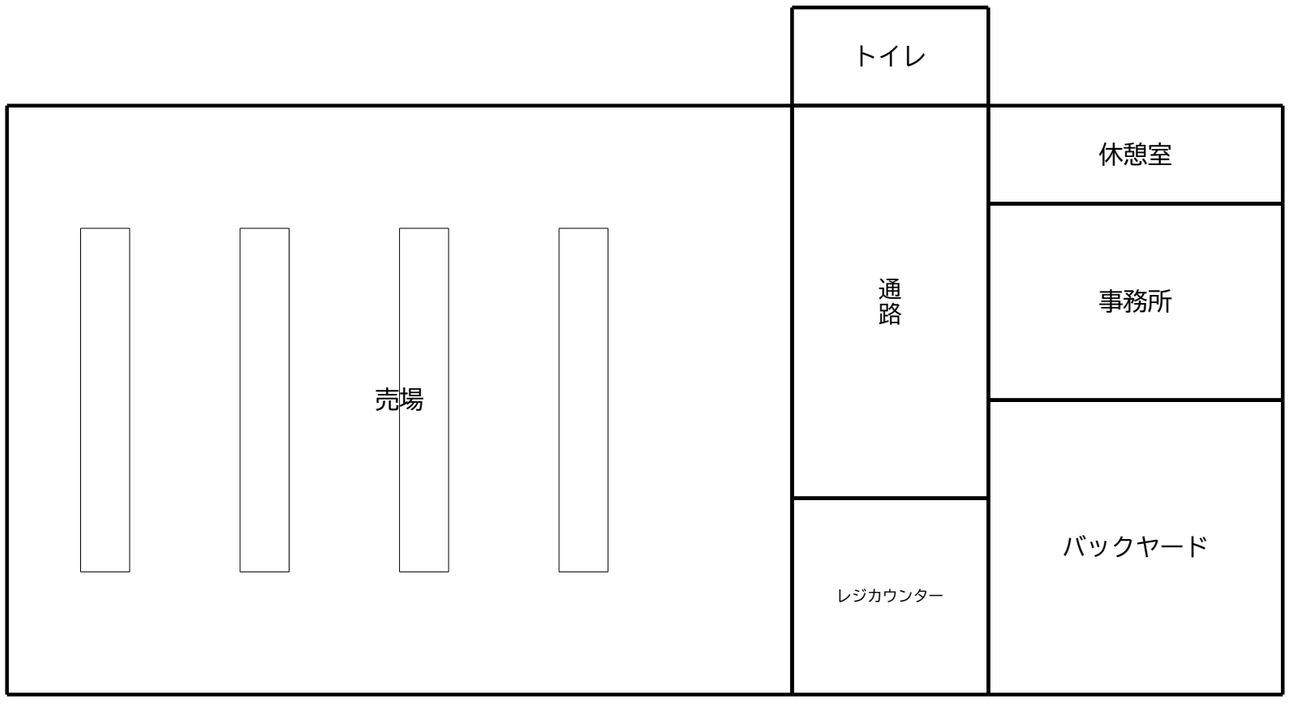

内装仕上平面図　S=1/100

工事名称	D商店内装工事
図面名称	内装仕上平面図
図番	I-02
縮尺	1/100
日付	2026.09.05
設計	サンプル内装設計